
※架空の見本です。実在の建物の図面ではありません。

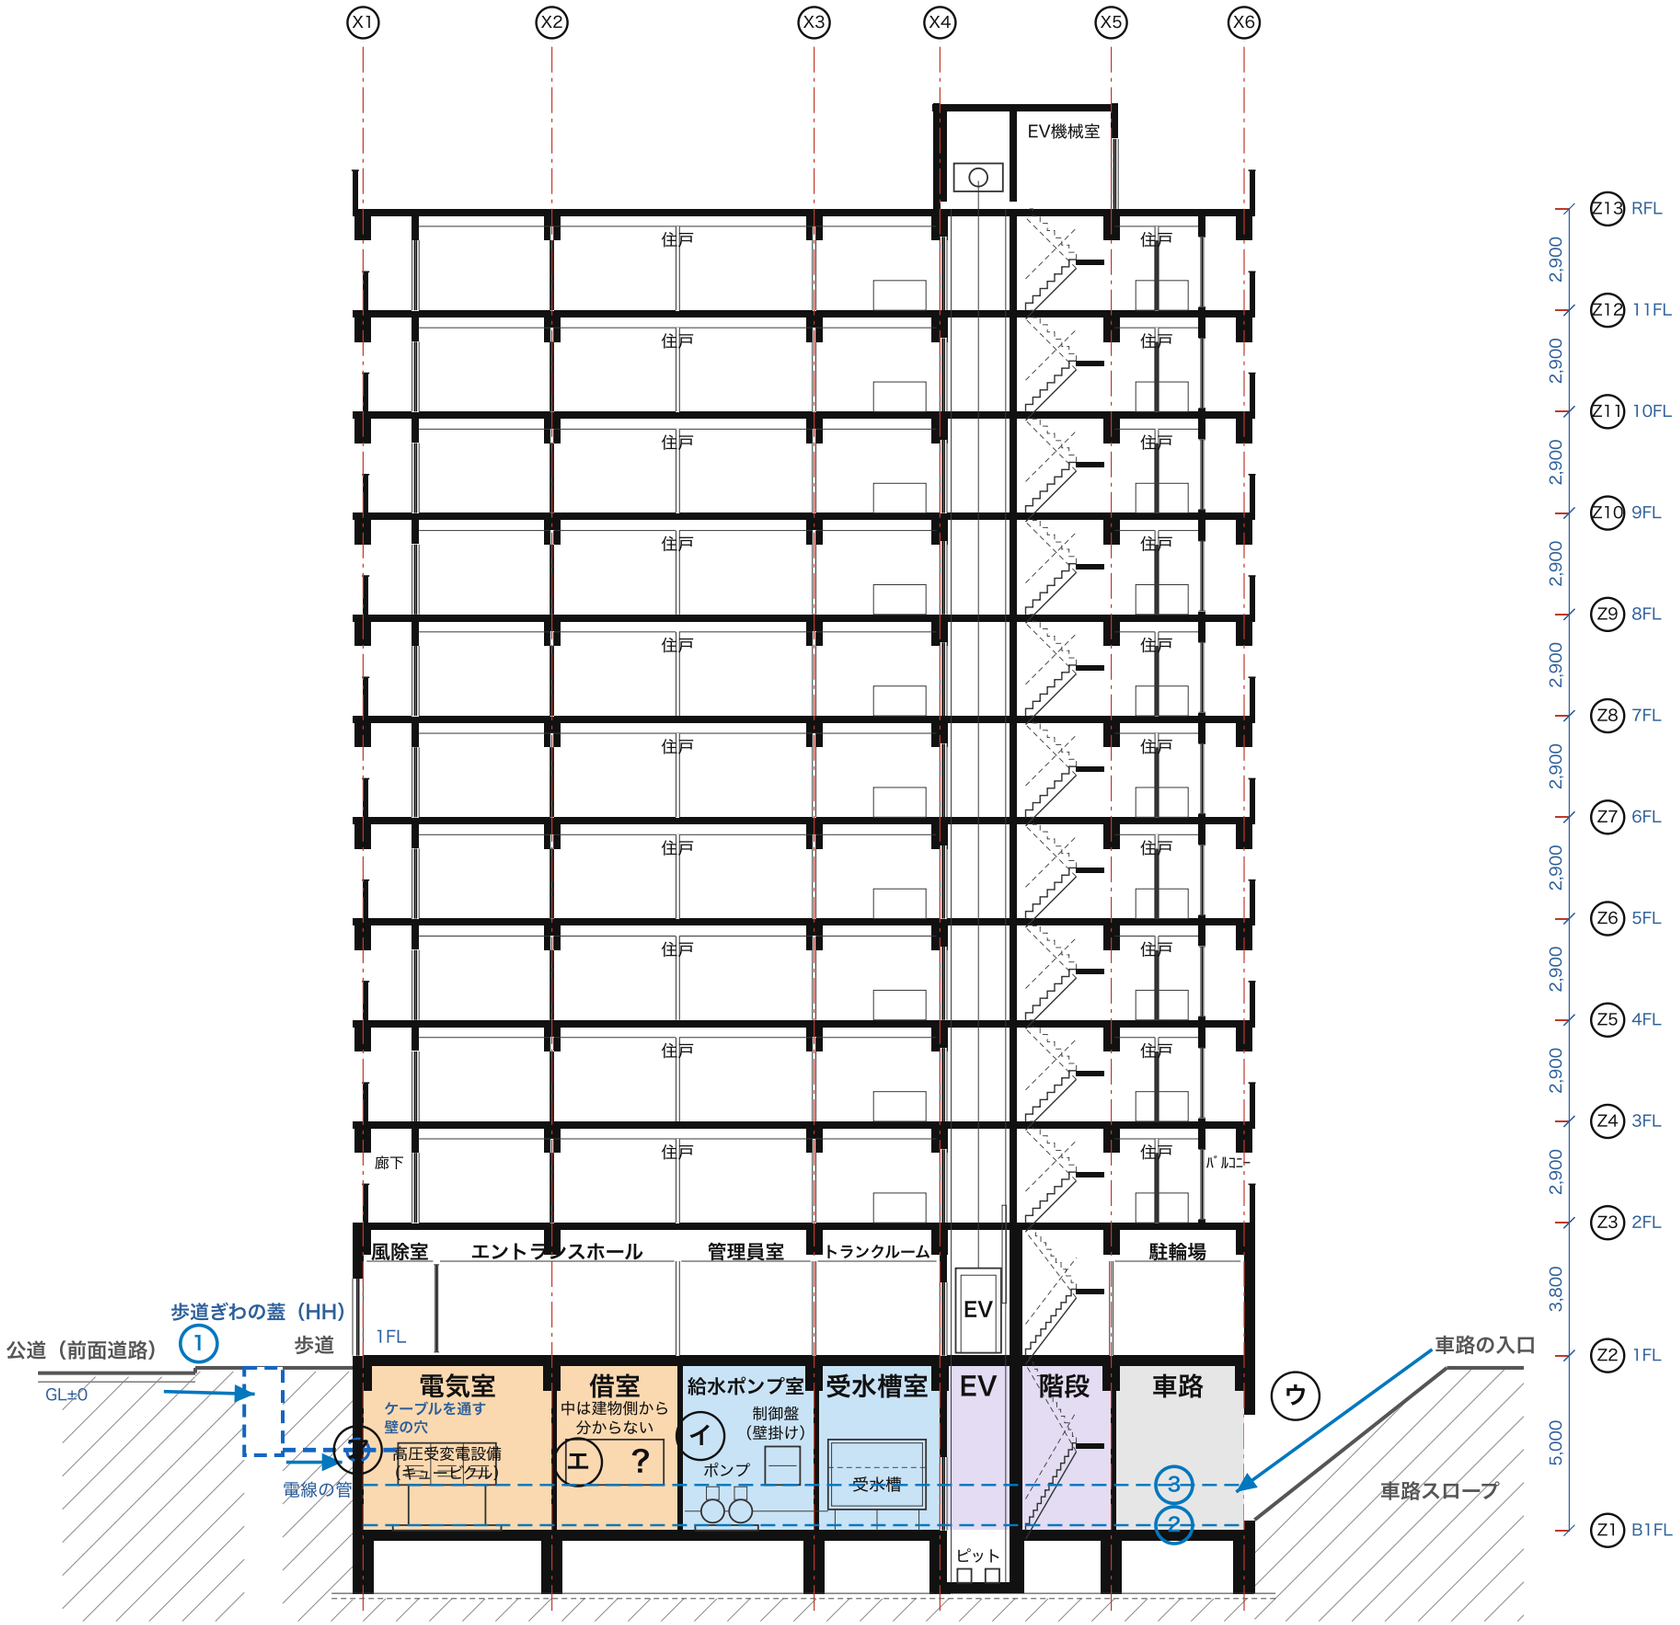

模式断面図（水の入り道）　機器の階は順に並べた展開

水の位置（画面の①②③）

① 道路・スロープ・壁の穴に達した
② 一番低い床に達した
③ 盤・高圧受変電設備の下端に達した

破線は模式。高さの値ではありません。
部屋ごとに同じ高さになるとは限りません。
借室の中の機器の高さは分かりません。
壁の穴の止水の有無は図から分かりません。

水の入り道

ア ケーブルを通す壁の穴
ウ 地下へ降りる車路スロープ

水に弱い設備

イ 給水ポンプ制御盤
エ 東京電力の変圧器の部屋

断面の記号

- 床スラブ・梁・柱・壁（躯体）
- 間仕切り・天井・家具
- 通り芯（X・Z）と階高（mm）
- 水の位置（模式の破線）

工事名称	うみかぜコート（架空） 新築工事
図面名称	竣工図 模式断面図（水の入り道）
縮尺	S=1/100（用紙に合わせて縮小）
図番	A-201