
※架空の見本です。実在の建物の図面ではありません。

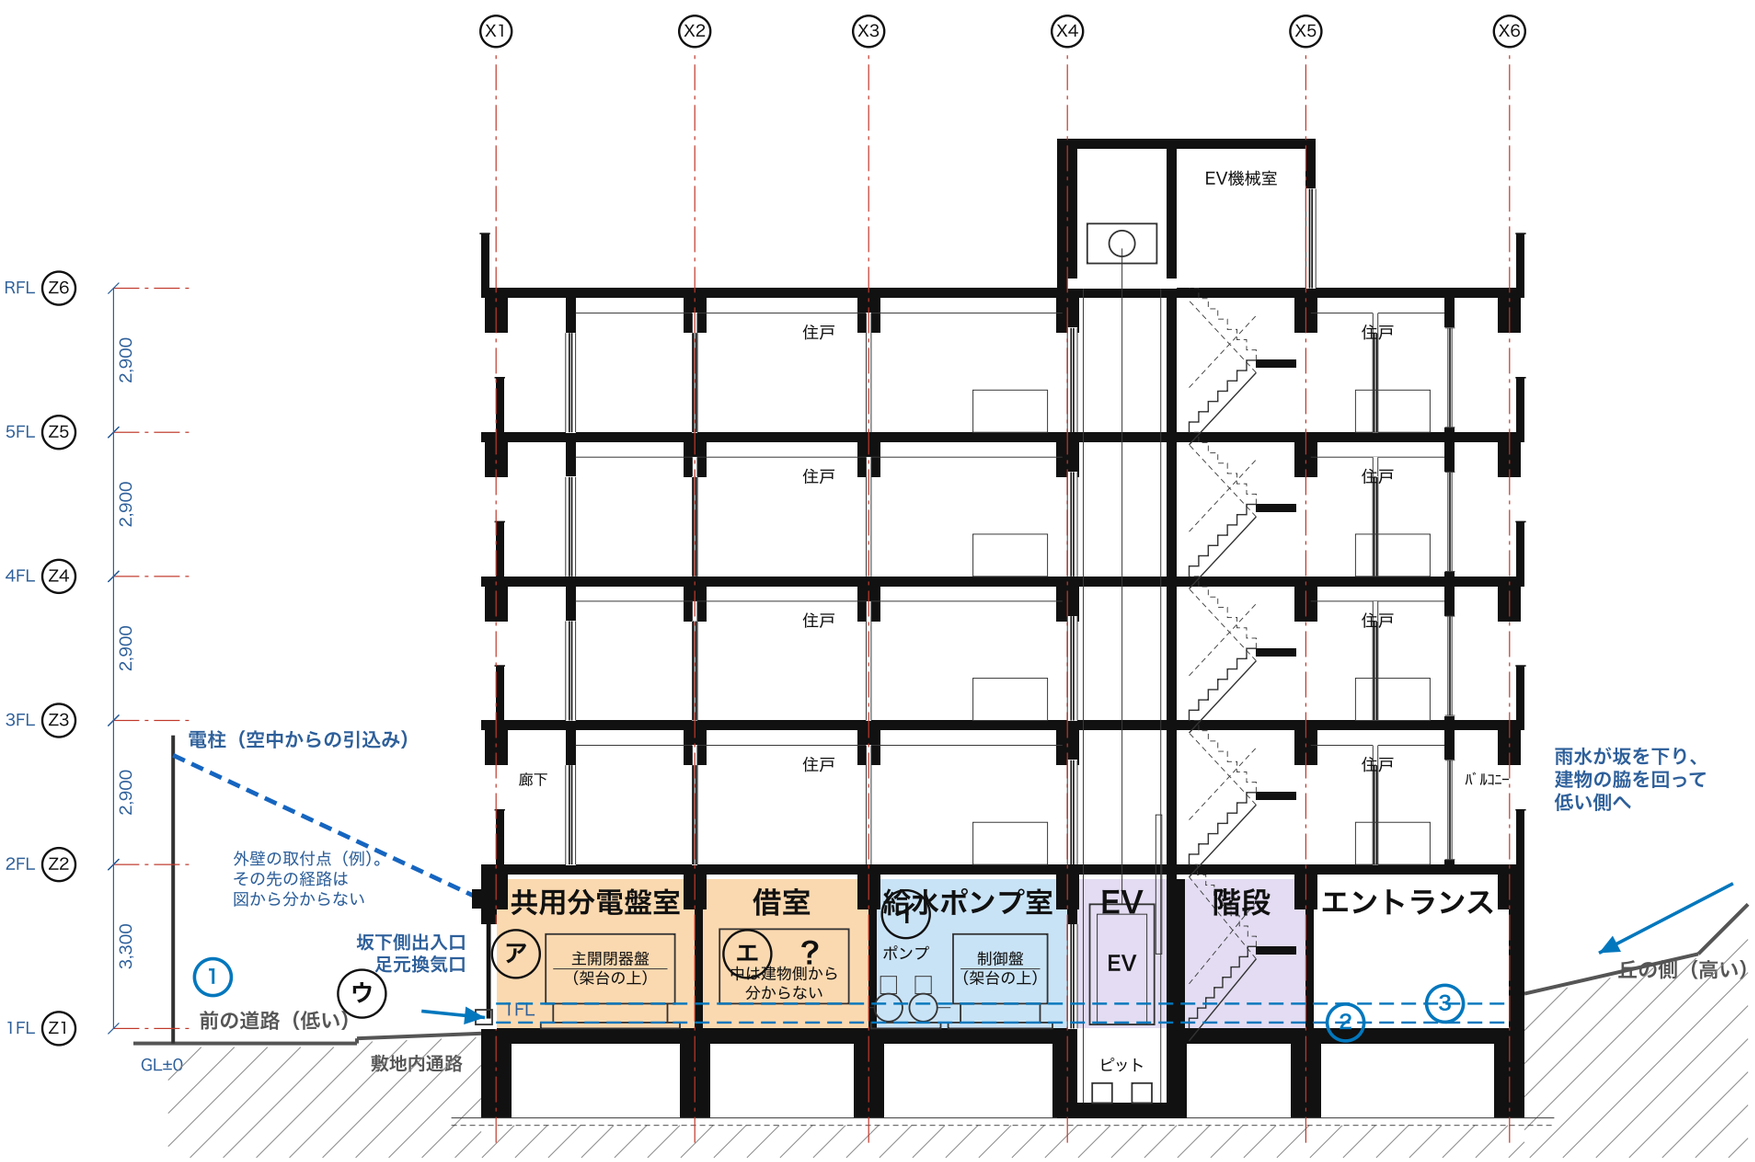

水の位置（画面の①②③）

1. 前の道路・坂下の扉に達した
2. 一番低い床に達した
3. 架台の上の盤の下端に達した

破線は模式。高さの値ではありません。
部屋ごとに同じ高さになるとは限りません。
借室の中の機器の高さは分かりません。

水の入り道

- ウ　坂の下の側の扉と足元の換気口

水に弱い設備

- ア　共用部の主開閉器盤
- イ　給水ポンプ制御盤
- エ　東京電力の変圧器の部屋

断面の記号

- 床スラブ・梁・柱・壁（躯体）
- 間仕切り・天井・家具
- 通り芯（X・Z）と階高（mm）
- 水の位置（模式の破線）

模式断面図（水の入り道）　機器の階は順に並べた展開

工事名称	たにとハイム（架空） 新築工事
図面名称	竣工図 模式断面図（水の入り道）
縮尺	S=1/100（用紙に合わせて縮小）
図番	A-211