
※架空の見本です。実在の建物の図面ではありません。

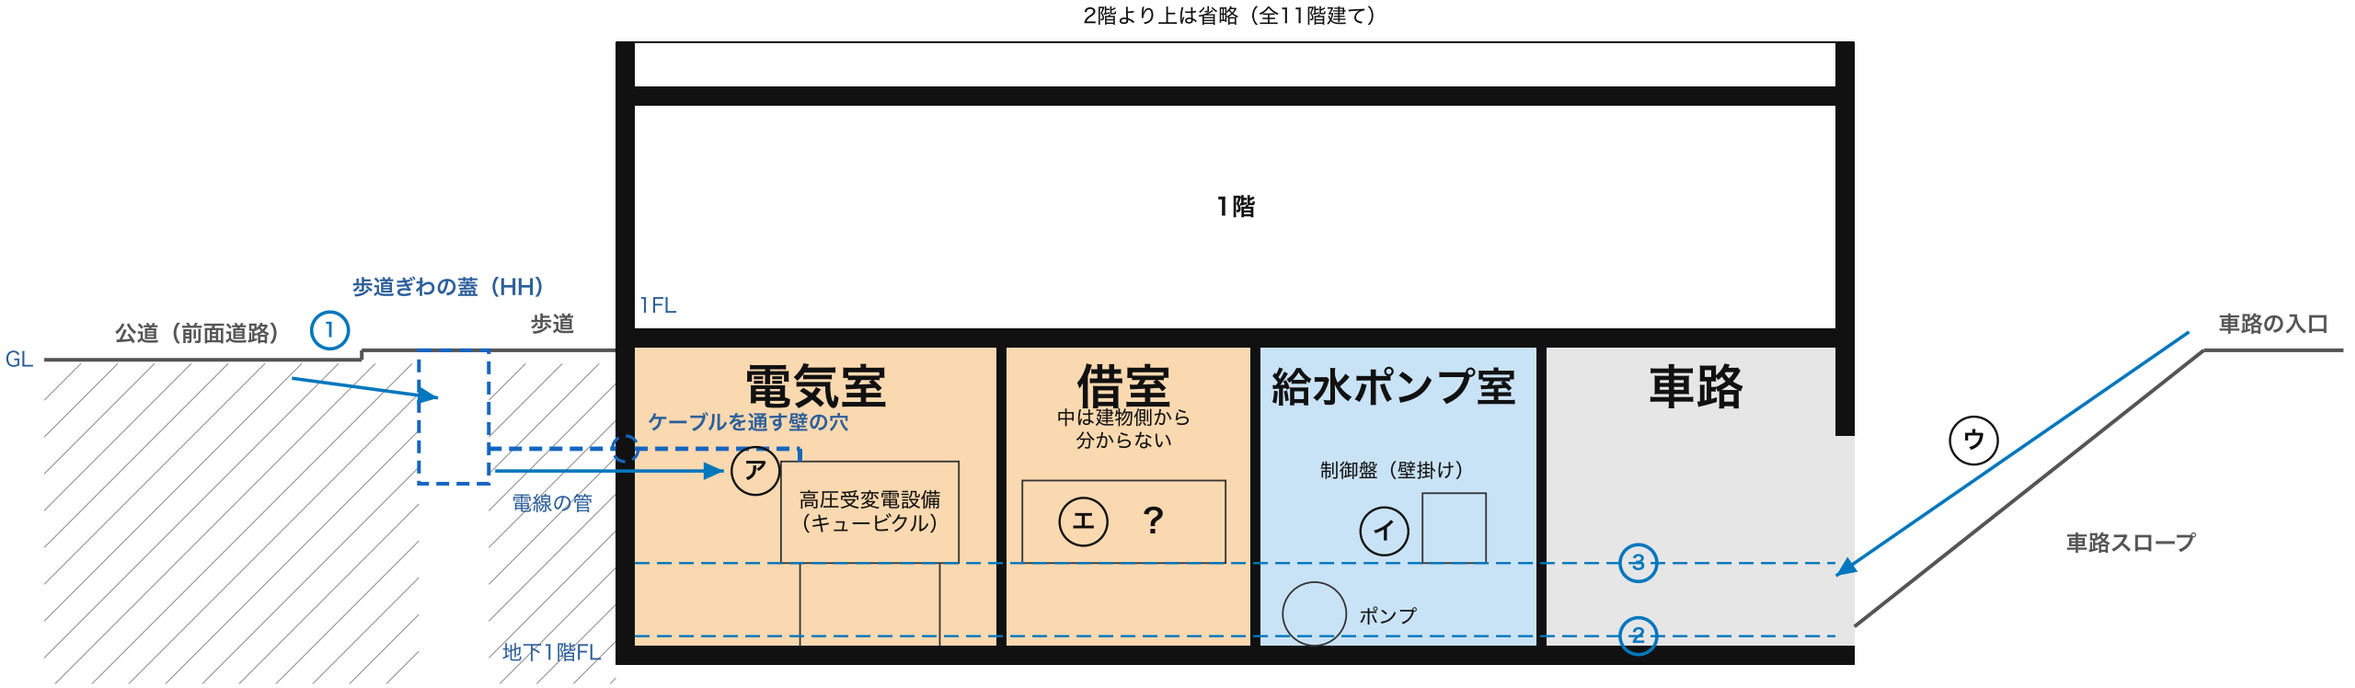


**模式断面図（水の入り道） 部屋は順に並べた展開**

**水の位置（画面の①②③）**

- ① 道路・スロープ・壁の穴に達した
- ② 一番低い床に達した
- ③ 盤・高圧受変電設備の下端に達した

**破線は模式。高さの値ではありません。**
部屋ごとに同じ高さになるとは限りません。
借室の中の機器の高さは分かりません。
壁の穴の止水の有無は図から分かりません。

**水の入り道**

- ア ケーブルを通す壁の穴
- ウ 地下へ降りる車路スロープ

**水に弱い設備**

- イ ポンプのスイッチ盤
- エ 東京電力の変圧器の部屋

| | |
|---|---|
| 工事名称 | うみかぜコート（架空） 新築工事 |
| 図面名称 | 竣工図 模式断面図（水の入り道） |
| 縮尺 | 模式 |
| 図番 | A-201 |