
※架空の見本です。実在の建物の図面ではありません。

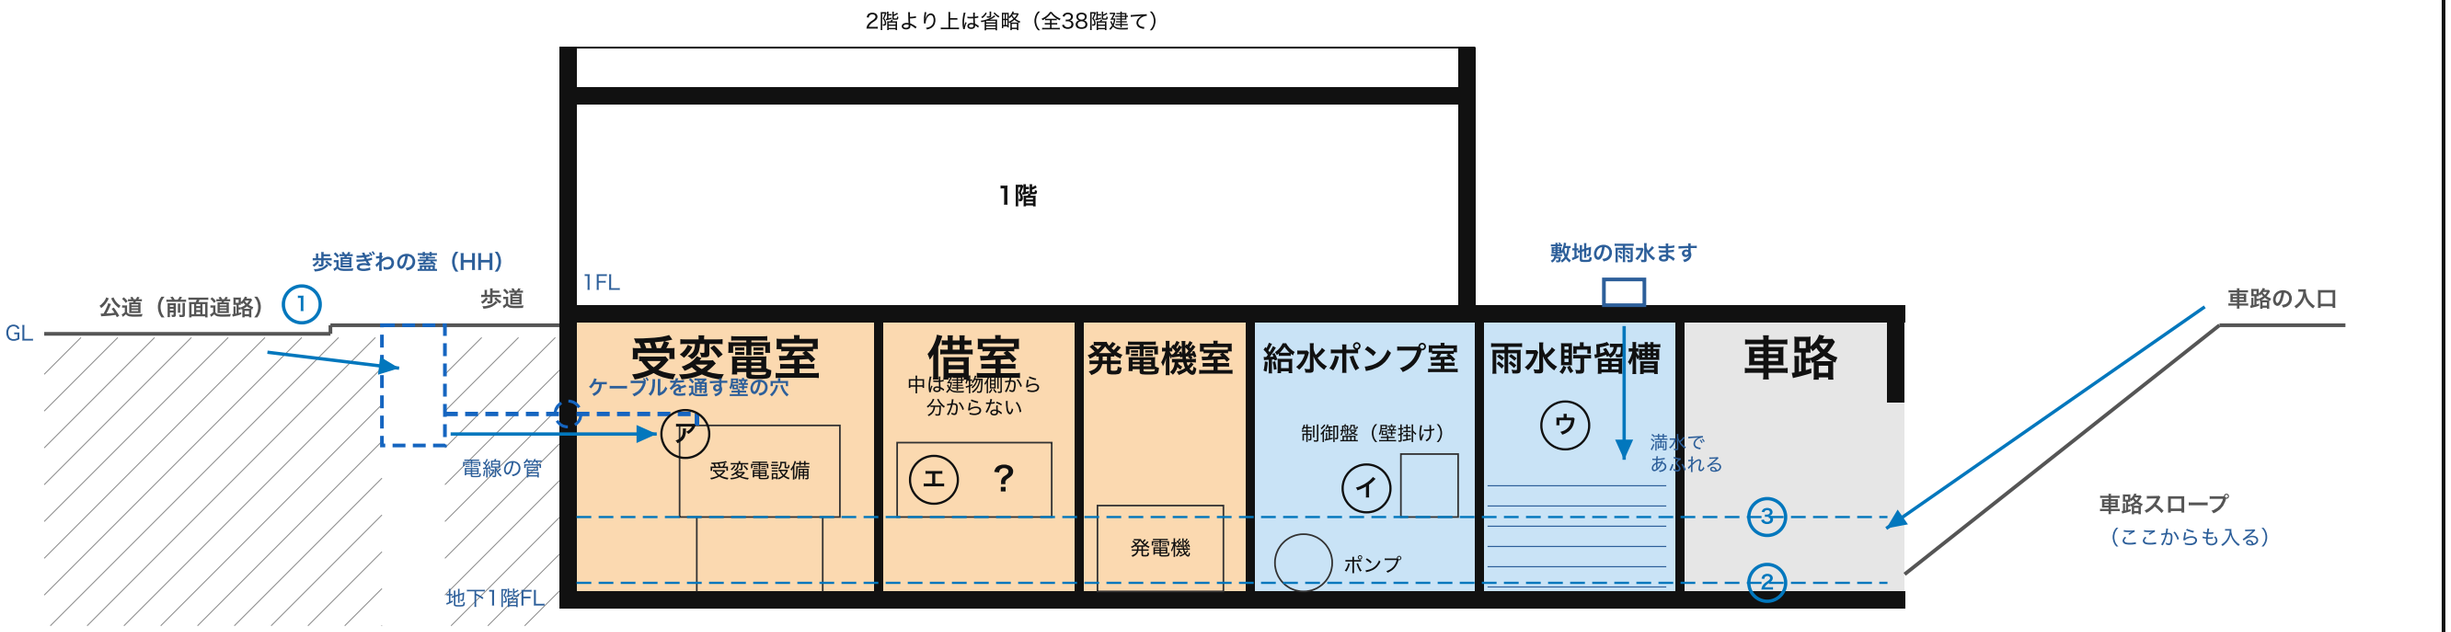

模式断面図（水の入り道）　部屋は順に並べた展開

水の位置（画面の①②③）

- ① 道路・スロープ・壁の穴に達した
- ② 一番低い床に達した
- ③ 盤・高圧受変電設備の下端に達した

破線は模式。高さの値ではありません。
部屋ごとに同じ高さになるとは限りません。
借室の中の機器の高さは分かりません。
壁の穴の止水の有無は図から分かりません。

水の入り道

- ア ケーブルを通す壁の穴
- ウ 雨水ますと地下の貯留タンク

水に弱い設備

- イ ポンプのスイッチ盤
- エ 東京電力の変圧器の部屋

工事名称	あおぞらタワー（架空） 新築工事
図面名称	竣工図 模式断面図（水の入り道）
縮尺	模式
図番	A-221