

※架空の見本です。実在の建物の図面ではありません。

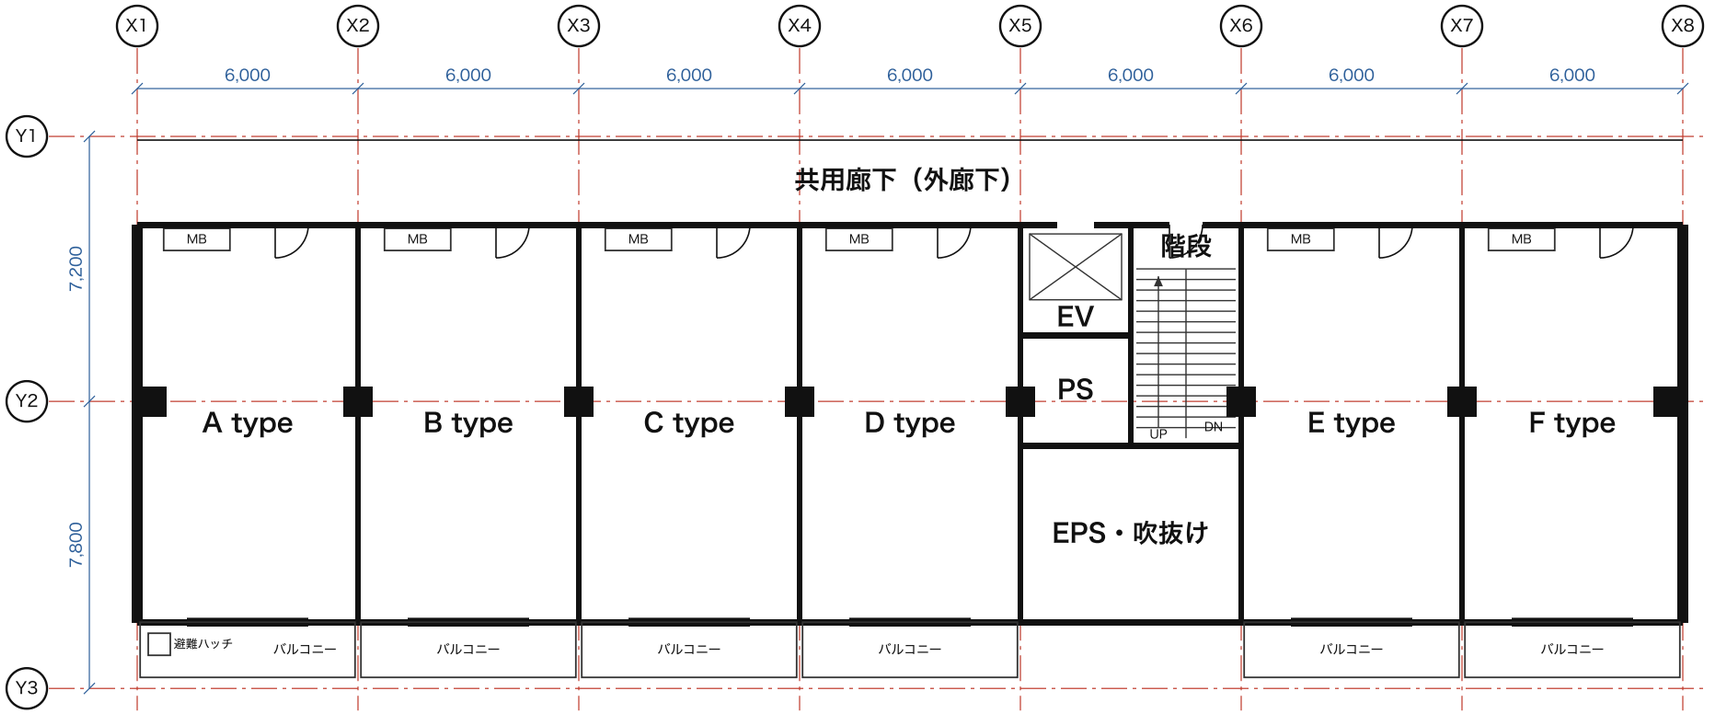

基準階平面図　S=1/100

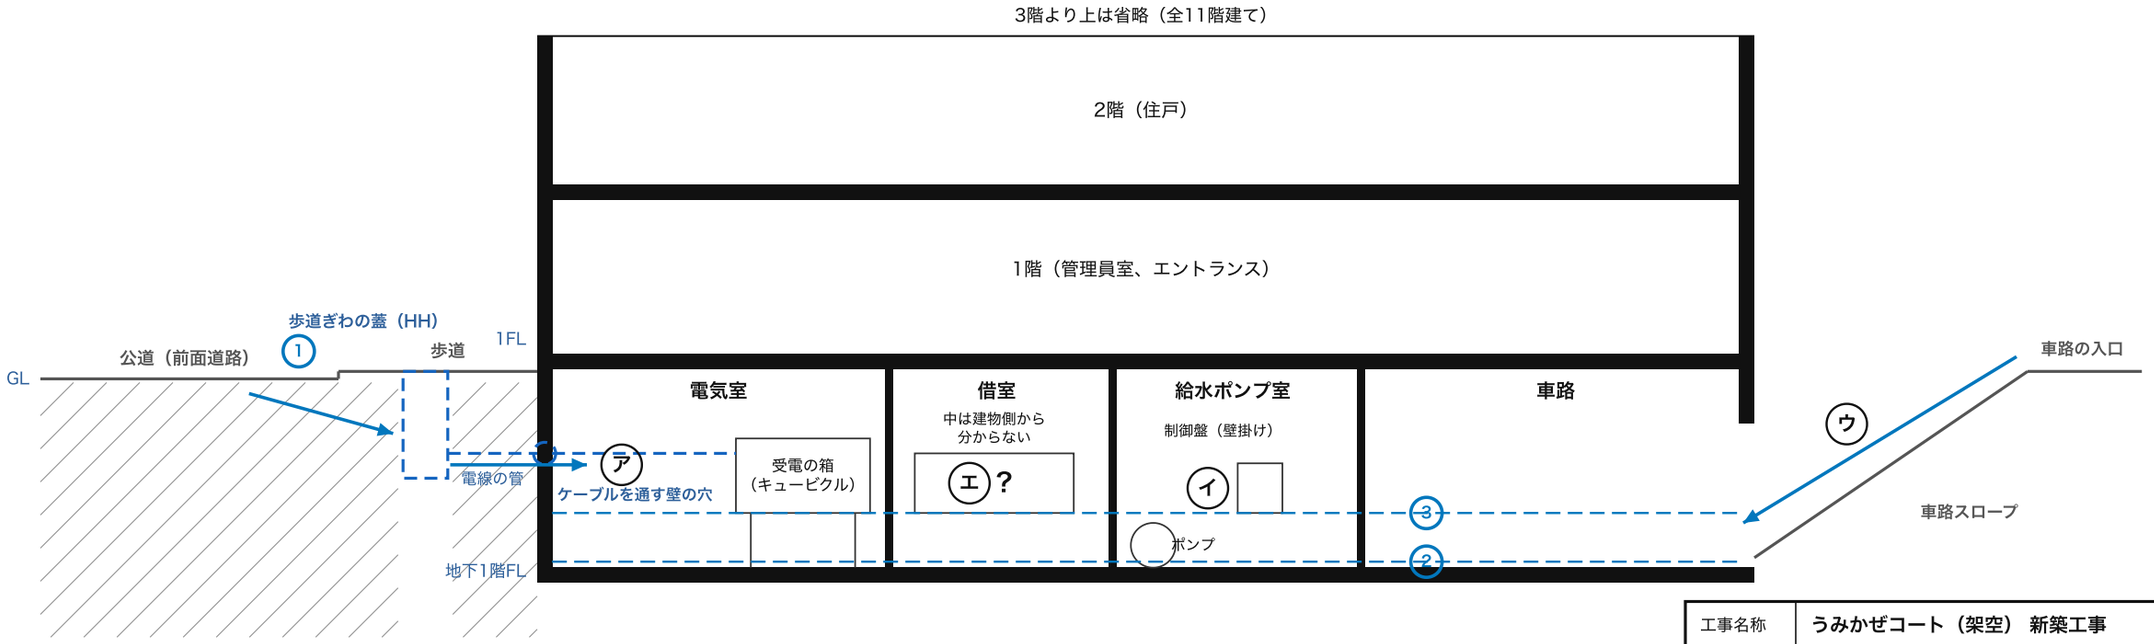

模式断面図（水の入り道）　部屋は順に並べた展開

N

水の位置（画面の①②③と同じ）

① 前の道路・スロープ・地下の壁の穴に達した

② 一番低い床（エレベーターの底の部分、床置きの機器の下端）に達した

③ 壁掛けや架台の上の盤、受電の箱、東京電力の変圧器の部屋の下端に達した

破線は模式で、高さの値ではありません。
全部の部屋が同じ高さになるという意味でもありません。

図の印

ア　ケーブルを通す壁の穴
イ　ポンプのスイッチ盤
ウ　地下へ降りる車路スロープ
エ　東京電力の変圧器の部屋

青の矢印は水の入り道です。青い文字は場所の名前です。
壁の穴の止水の有無は、この図から分かりません。
借室への引込みの経路は建物側から分からないので描いていません。
ポンプの盤が浸かると給水が止まります。受電の箱とは別のものです。
機器の構成は一例です。

工事名称	うみかぜコート（架空） 新築工事
図面名称	竣工図 基準階平面図・模式断面図（水の入り道）
縮尺	S=1/100、断面は模式
図番	A-201